
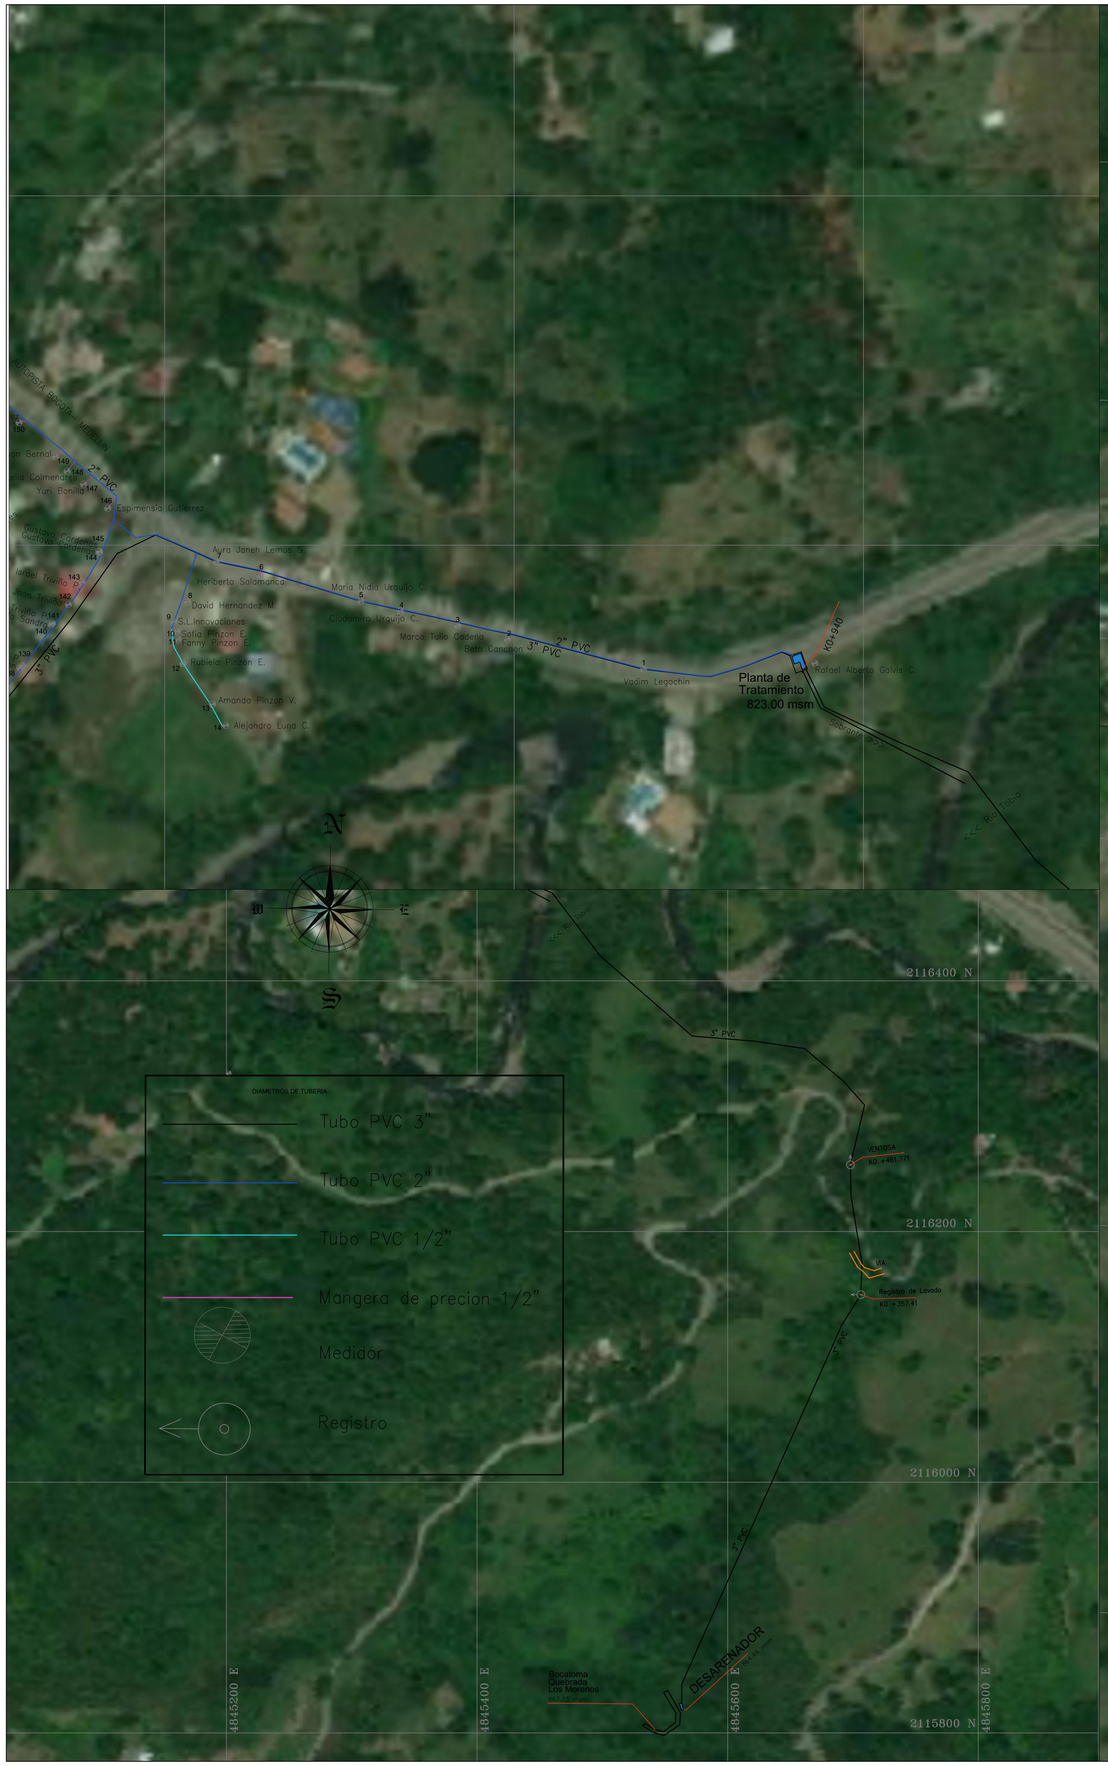


TOBIA CHICA

MUNICIPIO DE NOCAIMA
DEPTO DE CUNDINAMARCA
COLOMBIA
2024

ACUEDUCTO RURAL
CENTRO POBLADO
TOBIA CHICA

PLANO DE LOCALIZACIÓN
Escala 1 : 100.000

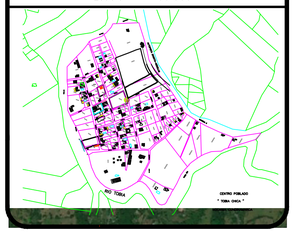

Leyenda

- Ramal de distribución
- Líneas Domiciliarias
- Lindero Veredal
- Numero de usuarios
- Ventosa
- Vías
- Residencial
- Institucional
- Comercial

ASOCIACIÓN DE USUARIOS DEL
SERVICIO DE ACUEDUCTO
CENTRO POBLADO
TOBIA CHICA

PLANTA DE ADUCCIÓN CONDUCCIÓN Y RED DE DISTRIBUCIÓN

Sistema de Coordenadas Planas, referidas al Dátum
MAGNA-SIRGAS-Origen Central-Norte Falso 2000000 m
Este Falso 5000000 m
Todas las distancias estan referidas en metros

Ing. Ambiental y Sanitaria
Universidad de La Salle
Angie Daniela Ortiz Rojas
Diego Cesar Plazas Cardona
Lina Vanesa Panqueva Miranda

ARCHIVO: ACU TOBIA.DWG	PLANO N° 2
ESCALA: 1 : 2500	
FECHA: JUNIO – 2022	